



CONCEPT, NOT FOR FABRICATION


REV	DESCRIPTION	DATE	BY
P1	Concept sheet	2026-09-25	AC

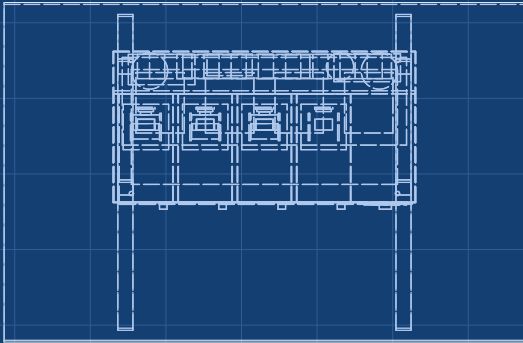


TOP VIEW
Scale 1:25

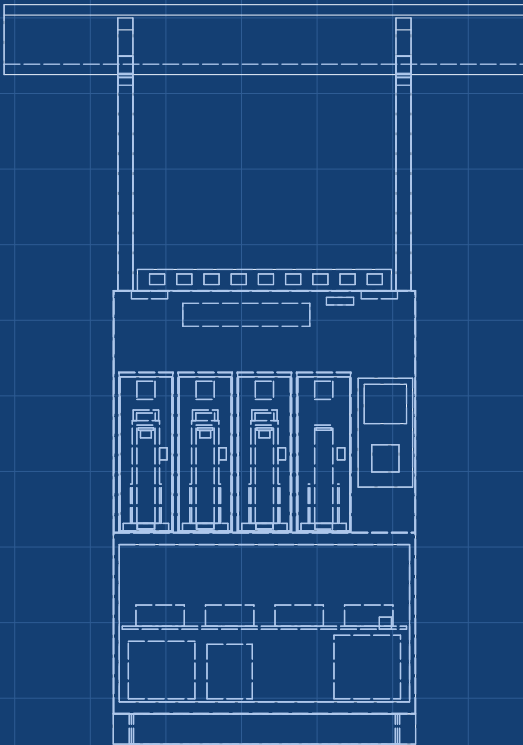

FRONT VIEW
Scale 1:25

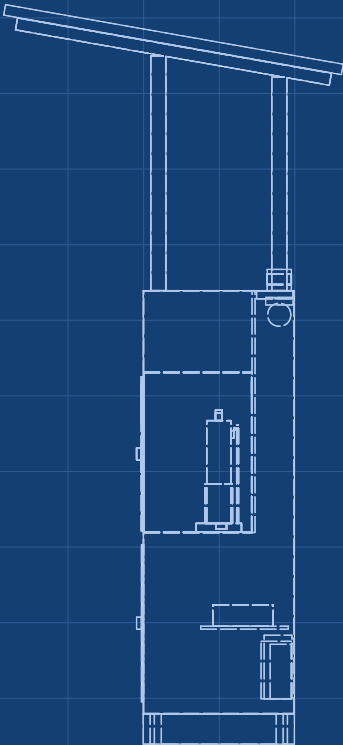

RIGHT VIEW
Scale 1:25

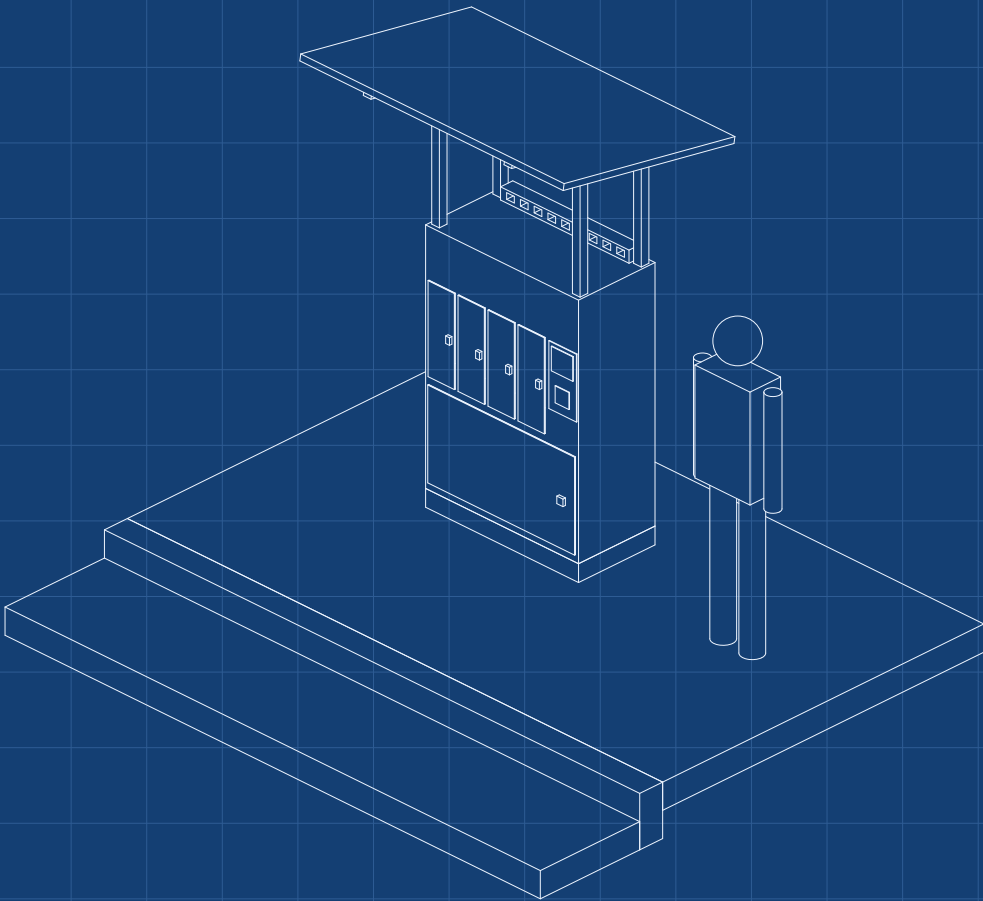

ISOMETRIC VIEW
Not to scale; figure is a 1.75 m person

KEY FIGURES

4 SwapCell v0.3 bays, 3 packs resident; swap about 31 s
Charge 20 to 80 % in 1.2 h, 15 to 100 % in 2.0 h
Peak grid draw 1.25 kW, single phase (est.)
20 swaps a day: 8.8 kWh grid, 0.77 kWh solar (est.)
Solar 9.3 % of charging energy (R6 not met)
1.0 x 0.5 m footprint, 2.45 m to canopy top

DOCKHUB

Street battery swap station concept

DRAWING NO.

DKH-DWG-010

REV

P1

SHEET

1 of 1

SIZE

ANSI B

SCALE

1:25

UNITS

mm

PROJECTION



DATE

2026-09-25

DRAWN

Amish Chadha

MATERIAL / NOTES

Massing model for concept communication